
PHASE-1

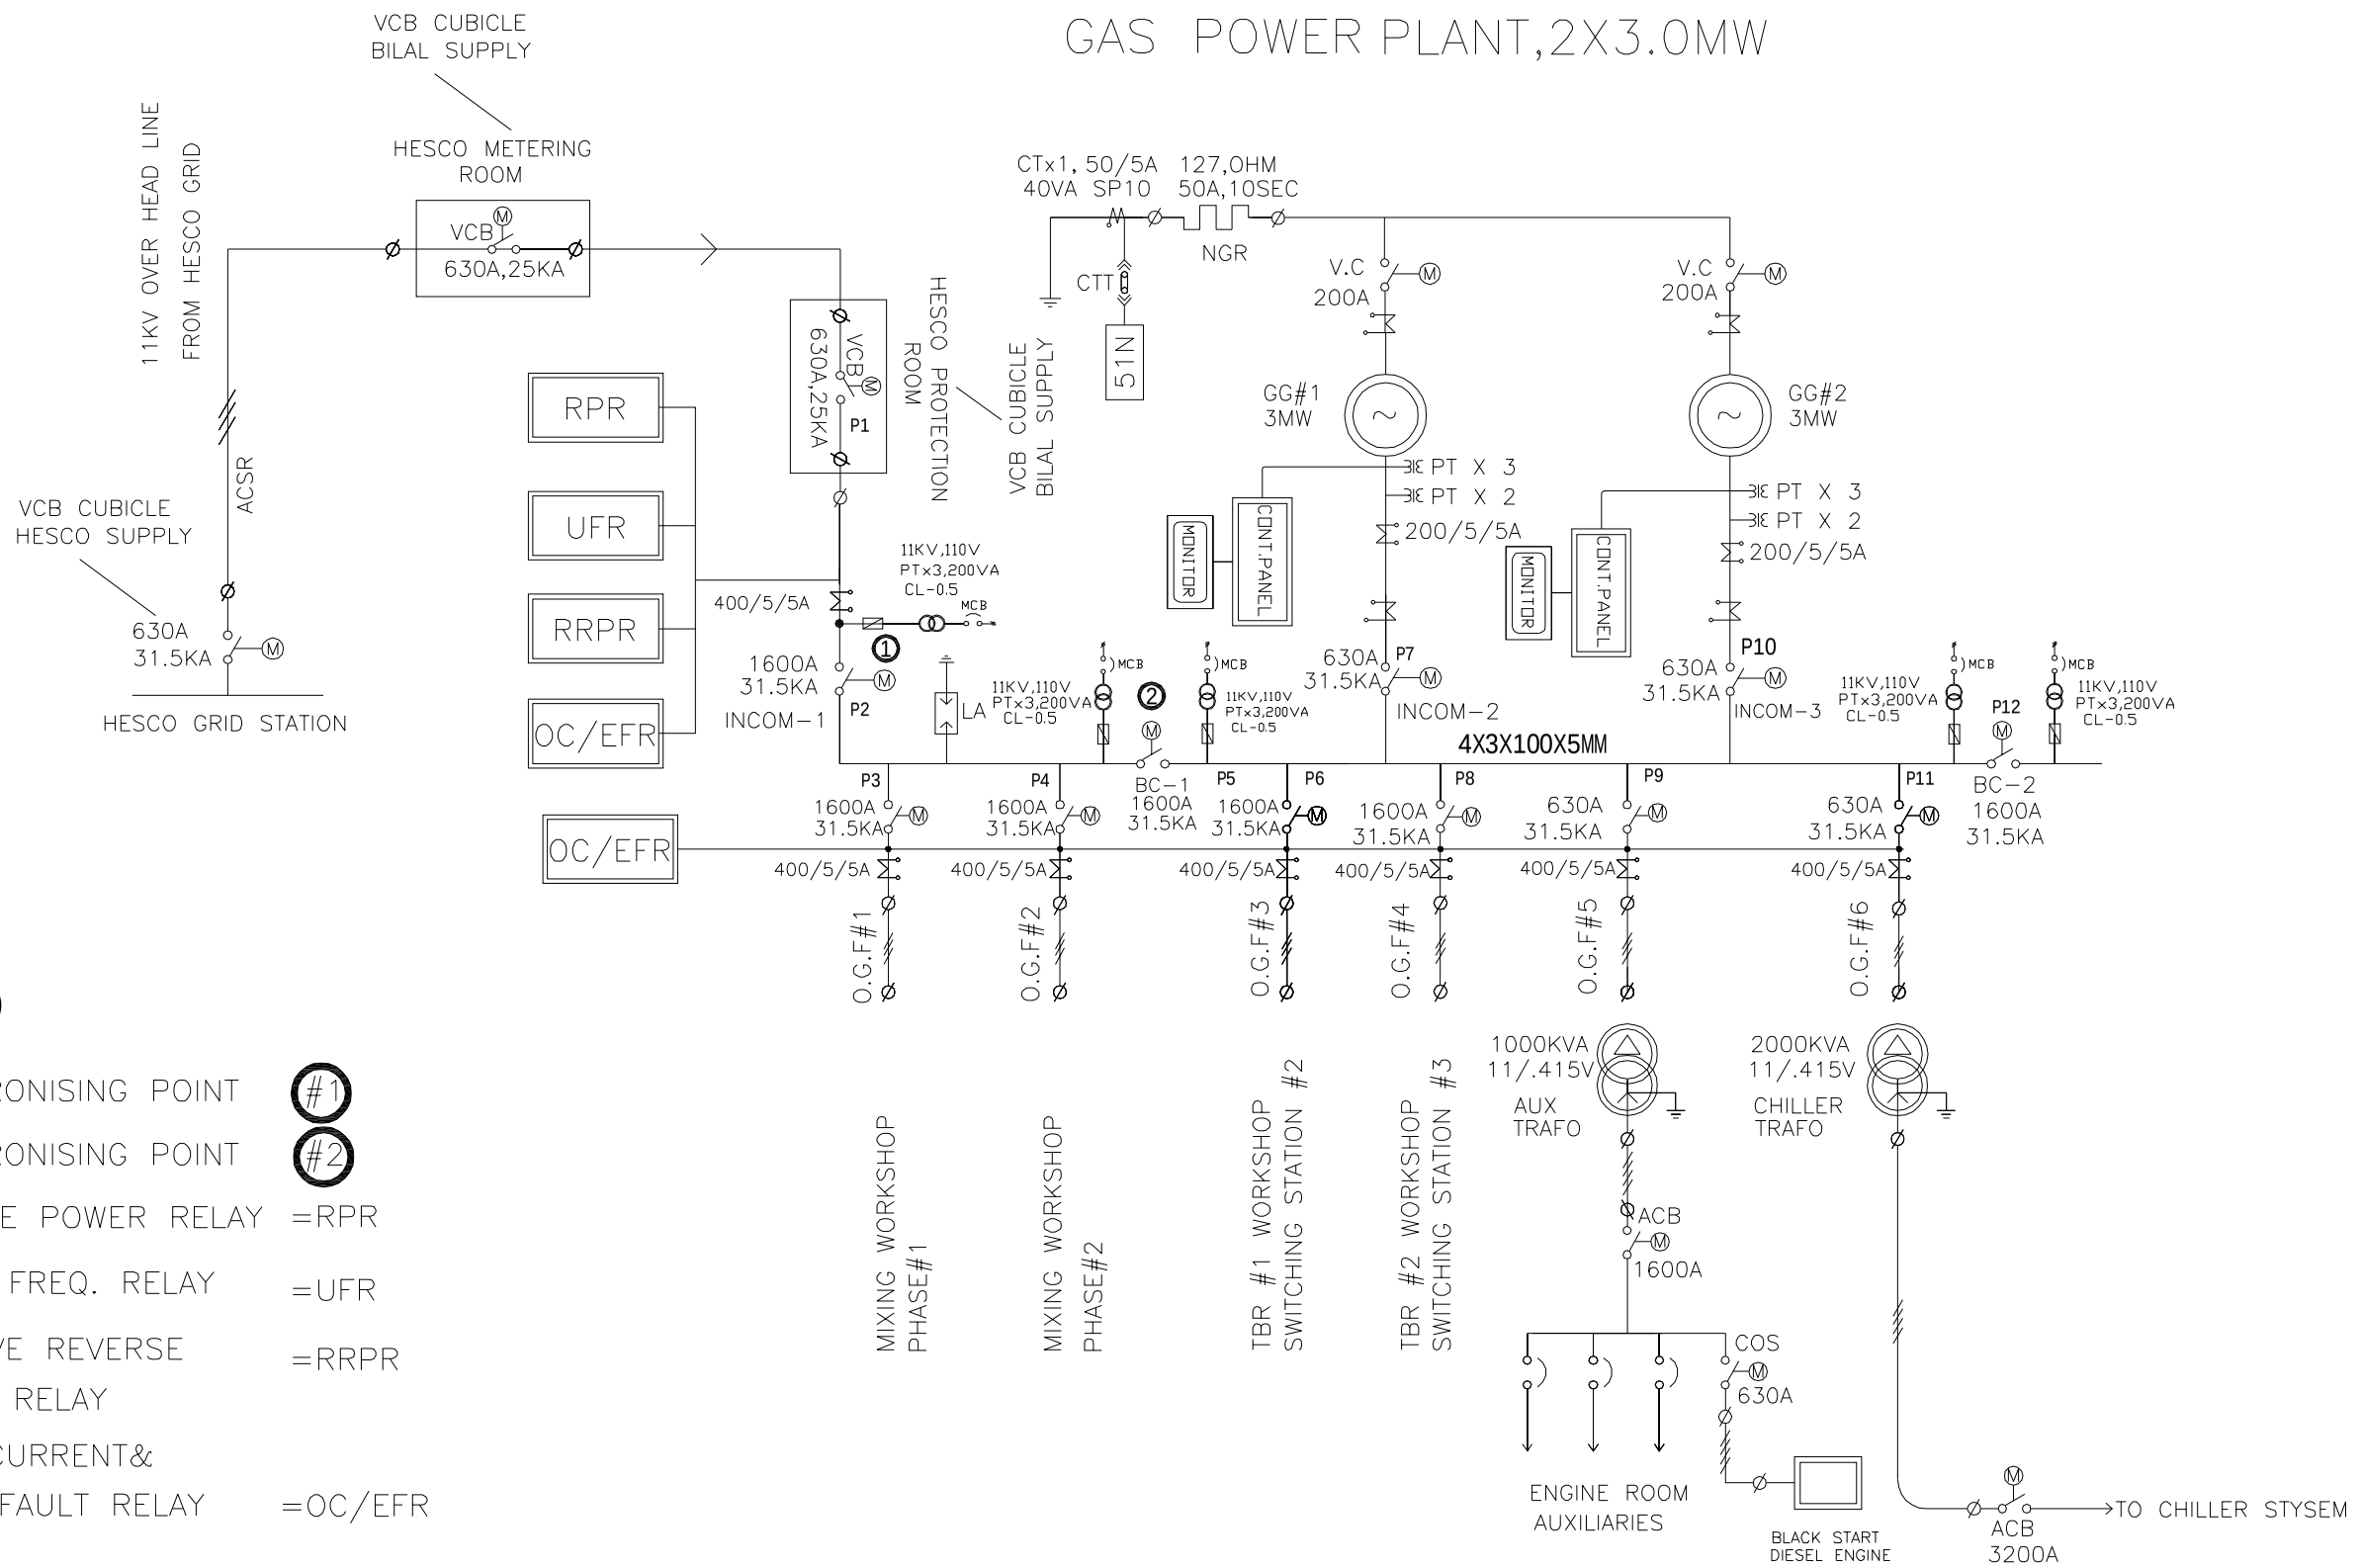

LEGEND

1 SYNCHRONISING POINT (#1)
2 SYNCHRONISING POINT (#2)
3 REVERSE POWER RELAY =RPR
4 UNDER FREQ. RELAY =UFR
5 REACTIVE REVERSE POWER RELAY =RRPR
6 OVER CURRENT& EARTH FAULT RELAY =OC/EFR

REV	DATE	REVISION
04		
03	21-06-2021	
02	06-01-2021	
01	29-12-2020	

POLYTEK ASSOCIATES (PVT) LIMITED
CONSULTING ENGINEERS
59-W, AIBAK BLOCK NEW GARDEN TOWN, LAHORE.
Ph.# 042-35866103,106,115
Fax. # 042-35866140
E-mail. polytek.associates@gmail.com

PROJECT: ***SERVIS LONG MARCH, NOORIABAD***

TITLE: ***S.L.D FOR GAS POWER PLANT &11KV GRID SUPPLY DISTRIBUTION SYSTEM (PHASE1,2,&3)***

DRAWN BY	M.K.K	DATE: 29-07-2020	SHEET	
DESIGNED BY	P. I. BUTT	SCALE:	01	
APPROVED BY	P. I. BUTT	DWG NO: PTK-SLM-SLD-001		