


SLM 40MW 132KVA HESCO GRID SLD

LEGENDS		
S.A	Surge Arrester	
C.T	Current Transformer	
P.T	Potential Transformer	
D.S	Disconnecter Switch/Isolator	
E.S	Earth Switch	
C.B	Circuit Breaker	

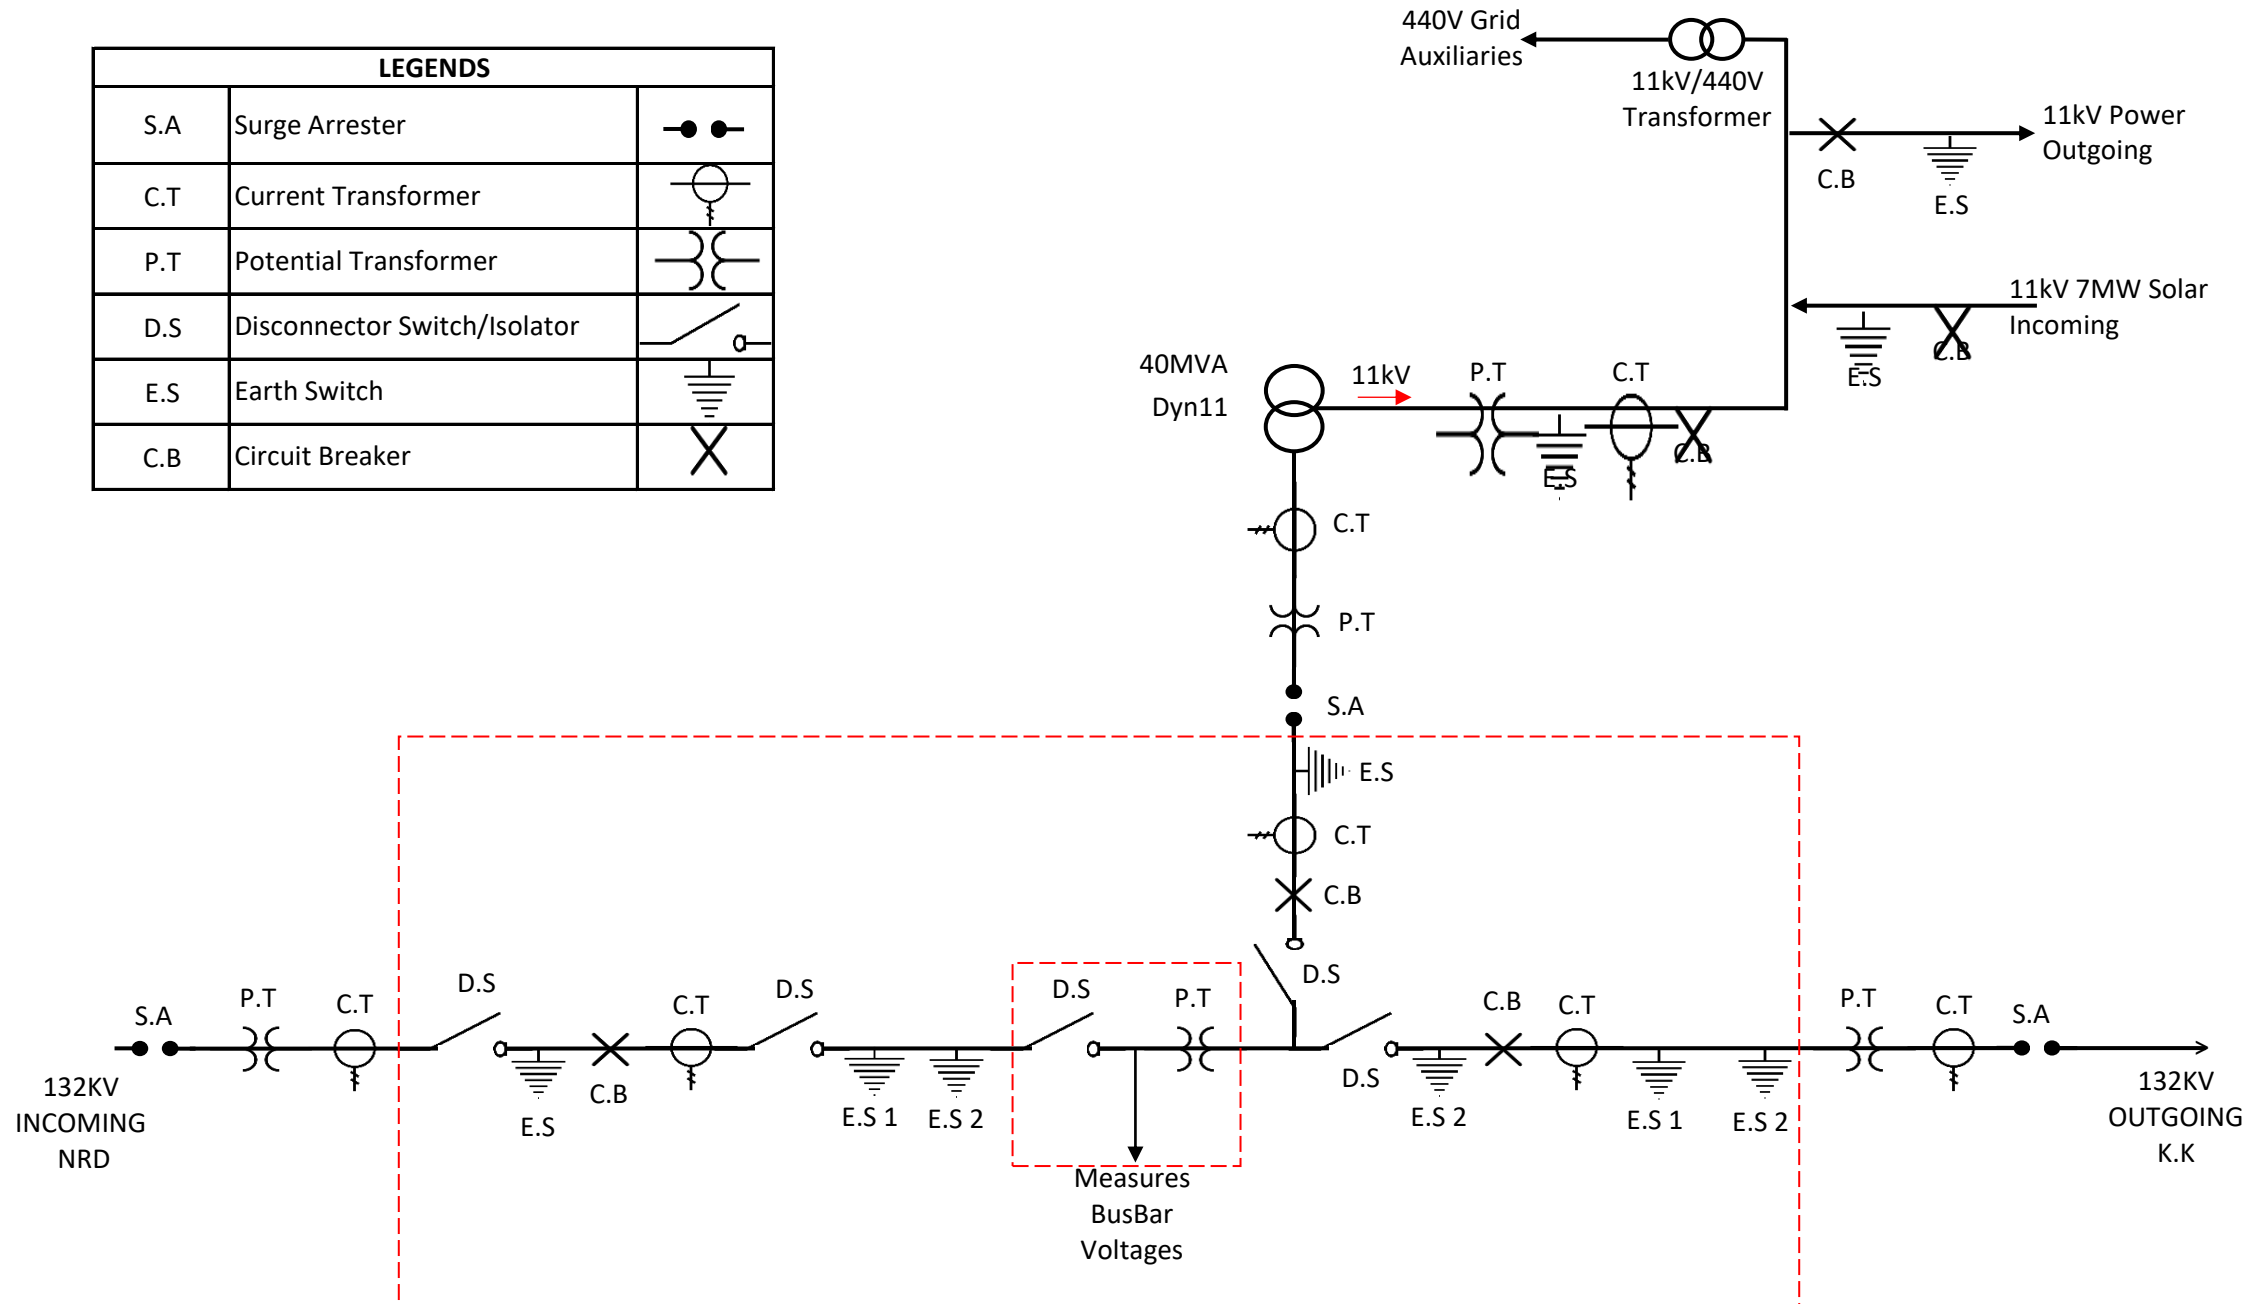

GIS Housing